

MrFlexySMPs Folded Horn Hybrid


Bauplan · Rev. B · 2026-10-16


Auf A3 in 100 % drucken (nicht „an Seite anpassen“). Alle Maße in mm.


3D-Modell (3dviewer.net):


Modelldateien (GitHub):

3D-Modell (3dviewer.net):	https://3dviewer.net/#model=https://raw.githubusercontent.com/SdWa5/3d/main/published/flexy-folded-horn-hybrid/flexy-folded-horn-hybrid.glb
Modelldateien (GitHub):	https://github.com/SdWa5/3d/tree/main/published/flexy-folded-horn-hybrid
Original-CAD (v28):	https://3dviewer.net/#model=https://github.com/Oletarier/bassw-rfel-folded-horn/blob/main/subwoofer%20v28.obj

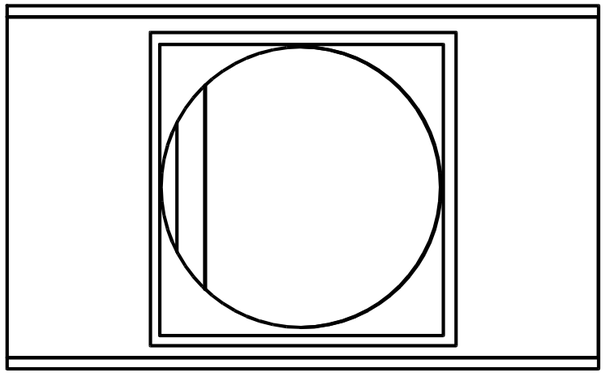


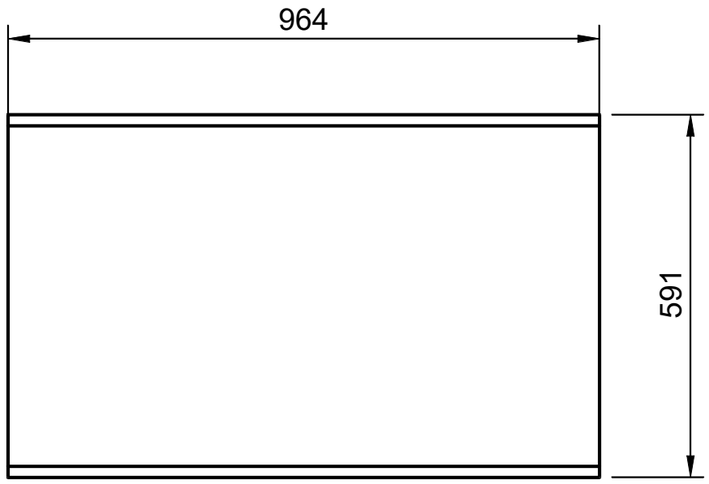

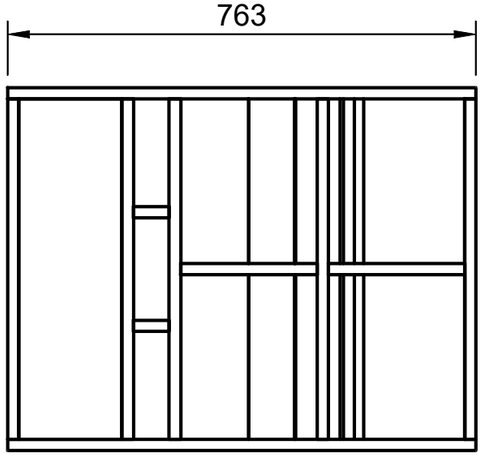


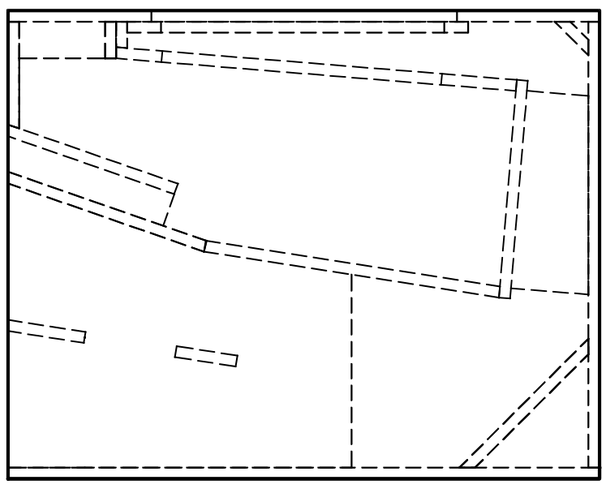


Abteilung	Technische Referenz	Erstellt von	Freigegeben von
SdWa5	Maßstab 1:10 auf A3	Oliver Ripper 25.02.2022	Stefan Ripper
		Dokumentart: Bauplan	Dokumentstatus: überarbeitet
		Titel: MrFlexySMPs Folded Horn Hybrid **Gesamtansichten**	Zeichnungsnr.: FLEXY-02
			Rev.: B · Ausgabedatum: 2026-10-16 · Blatt: 2/25

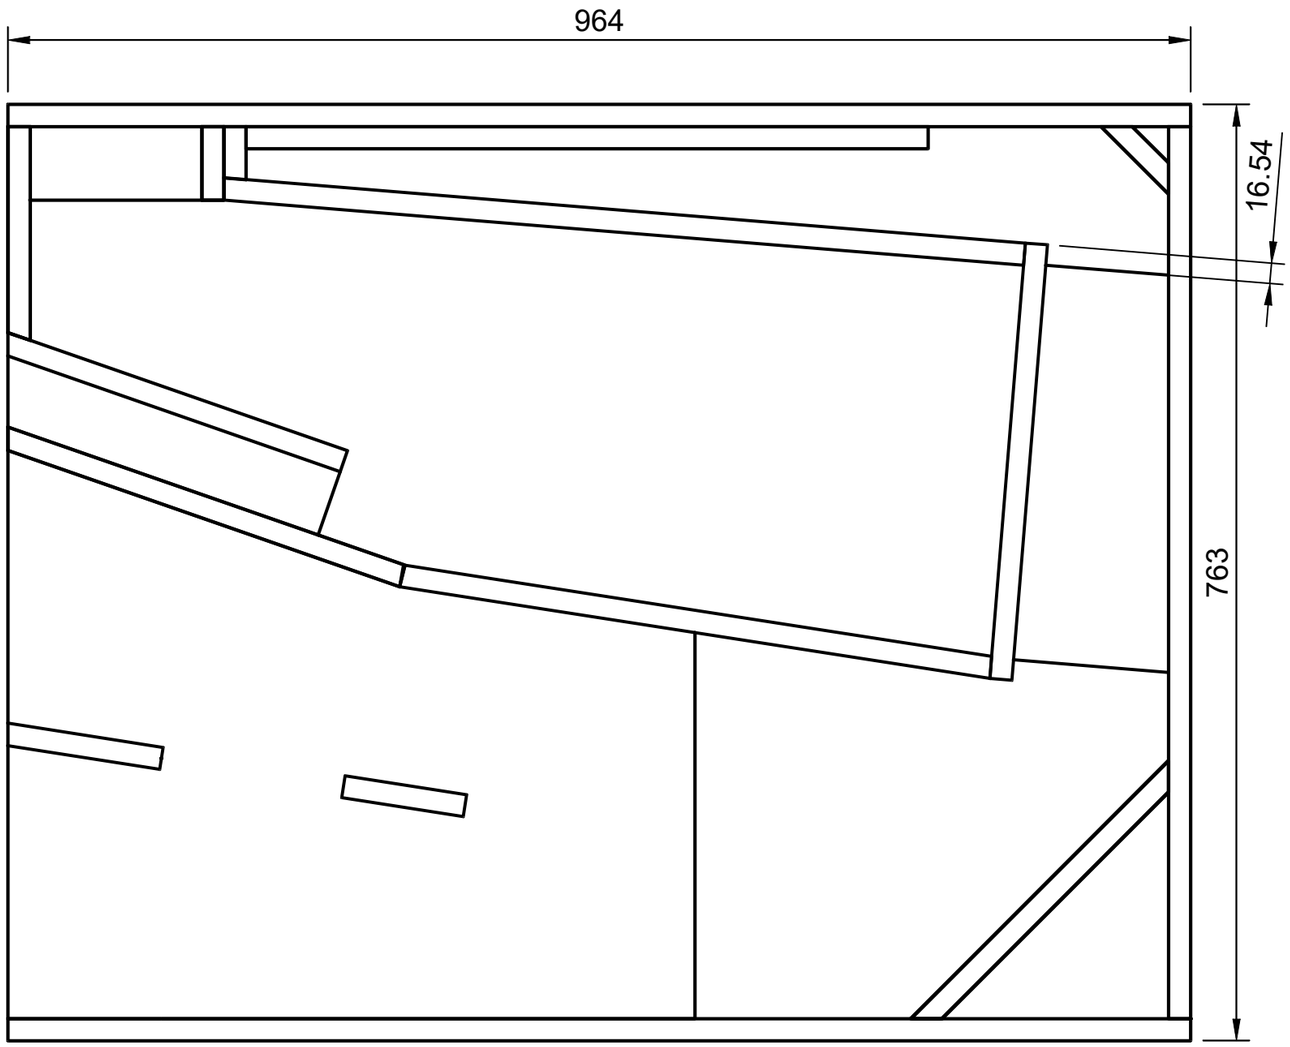

Abteilung: SdWa5	Technische Referenz: Maßstab 1:5 auf A3	Erstellt von: Oliver Ripper 25.02.2022	Freigegeben von: Stefan Ripper
		Dokumentart: Bauplan	Dokumentstatus: überarbeitet
		Titel: MrFlexySMPs Folded Horn Hybrid **Seitenschnitt**	Zeichnungsnr.: FLEXY-03
			Rev.: B / Ausgabedatum: 2026-10-16 / Blatt: 3/25

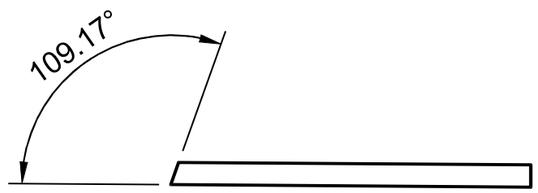


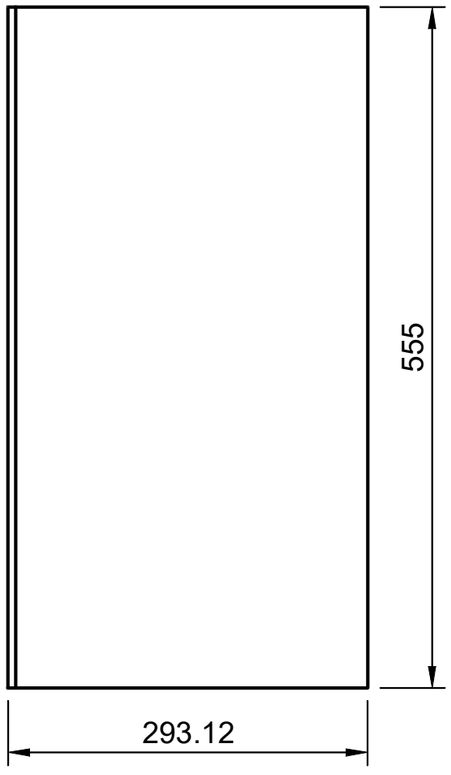

Abteilung: SdWa5	Technische Referenz: Maßstab 1:5 auf A3	Erstellt von: Oliver Ripper 25.02.2022	Freigegeben von: Stefan Ripper
		Dokumentart: Bauplan	Dokumentstatus: überarbeitet
		Titel: MrFlexySMPs Folded Horn Hybrid **Platte 555 × 293,12**	Zeichnungsnr.: FLEXY-04
			Rev.: B / Ausgabedatum: 2026-10-16 / Blatt: 4/25

HINWEIS


Gleicher Zuschnitt wie die Deckplatte (Blatt 6).

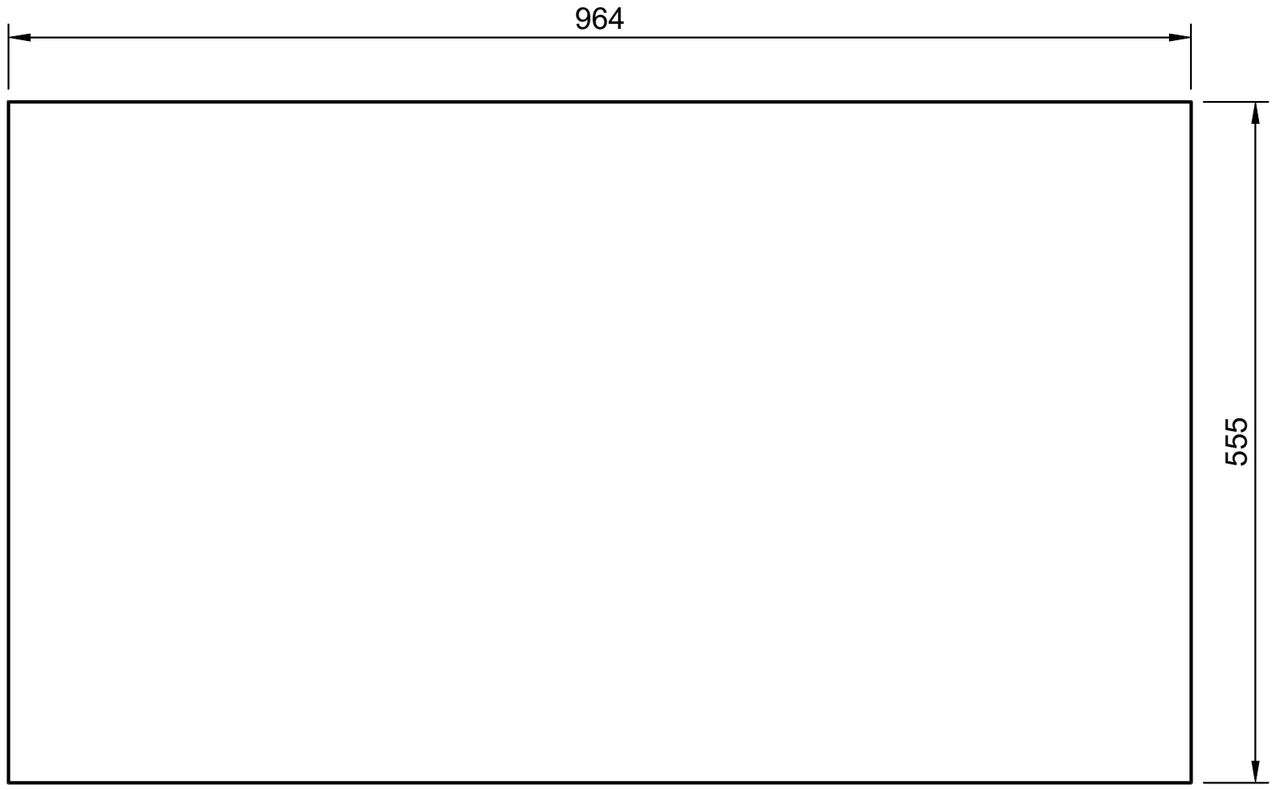

Abteilung: SdWa5	Technische Referenz: Maßstab 1:5 auf A3	Erstellt von: Oliver Ripper 25.02.2022	Freigegeben von: Stefan Ripper
		Dokumentart: Bauplan	Dokumentstatus: überarbeitet
		Titel: MrFlexySMPs Folded Horn Hybrid **Bodenplatte 964 × 555**	Zeichnungsnr.: FLEXY-05
			Rev.: B / Ausgabedatum: 2026-10-16 / Blatt: 5/25

HINWEIS


Das ausgeschnittene Stück ergibt den Deckel (Blatt 14).

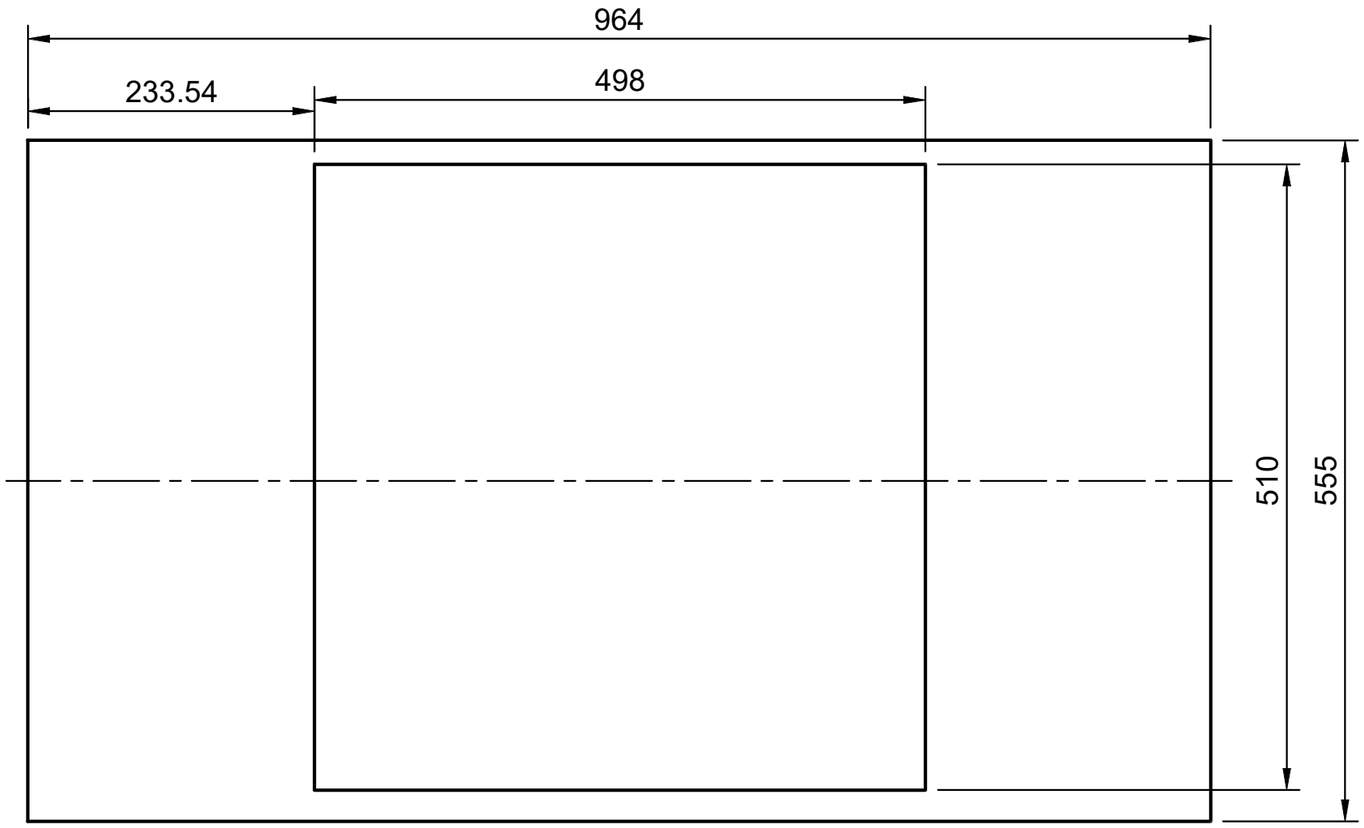

Abteilung: SdWa5	Technische Referenz: Maßstab 1:5 auf A3	Erstellt von: Oliver Ripper 25.02.2022	Freigegeben von: Stefan Ripper
		Dokumentart: Bauplan	Dokumentstatus: überarbeitet
		Titel: MrFlexySMPs Folded Horn Hybrid **Deckplatte mit Deckelausschnitt**	Zeichnungsnr.: FLEXY-06
			Rev.: B / Ausgabedatum: 2026-10-16 / Blatt: 6/25


OPTIONAL

Der Rahmen kann auch aus vier einzelnen Latten (Verschnitt) gebaut werden.

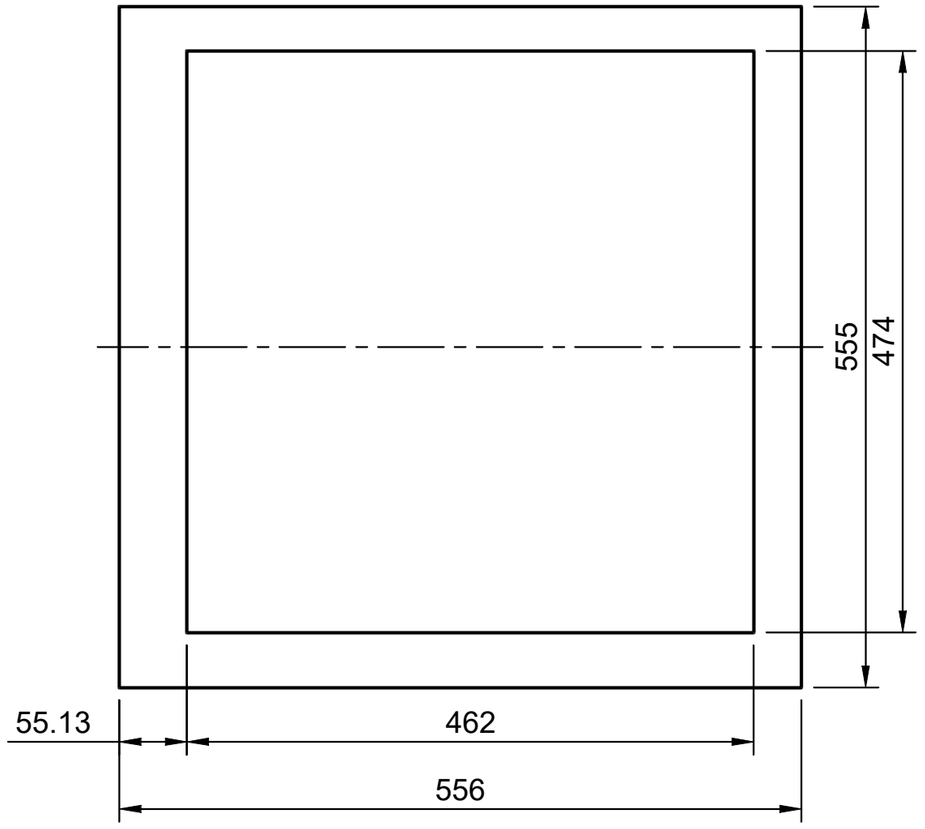

Abteilung: SdWa5	Technische Referenz: Maßstab 1:5 auf A3	Erstellt von: Oliver Ripper 25.02.2022	Freigegeben von: Stefan Ripper
		Dokumentart: Bauplan	Dokumentstatus: überarbeitet
		Titel: MrFlexySMPs Folded Horn Hybrid **Rahmen 556 × 555**	Zeichnungsnr.: FLEXY-07
			Rev.: B / Ausgabedatum: 2026-10-16 / Blatt: 7/25


x2

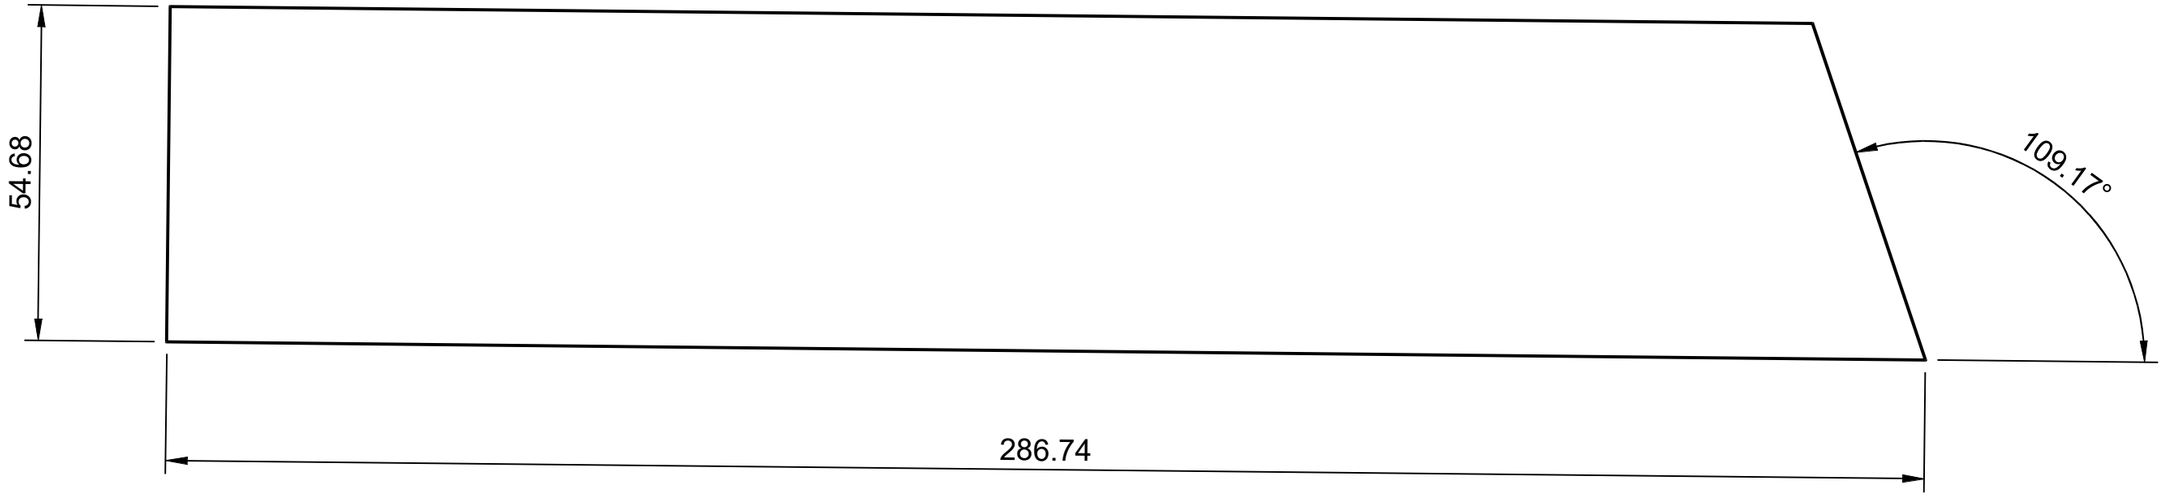

Abteilung	Technische Referenz	Erstellt von	Freigegeben von
SdWa5	Maßstab 1:1 auf A3	Oliver Ripper 25.02.2022	Stefan Ripper
		Dokumentart: Bauplan	Dokumentstatus: überarbeitet
		Titel: MrFlexySMPs Folded Horn Hybrid **Trapezleiste 286,74 (2×)**	Zeichnungsnr.: FLEXY-08
			Rev.: B · Ausgabedatum: 2026-10-16 · Blatt: 8/25

OPTIONAL


Verstrebungen: können z. B. auch aus Metall gefertigt werden.

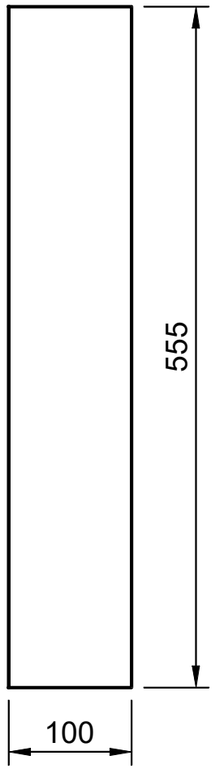


Abteilung	Technische Referenz	Erstellt von	Freigegeben von
SdWa5	Maßstab 1:5 auf A3	Oliver Ripper 25.02.2022	Stefan Ripper
		Dokumentart: Bauplan	Dokumentstatus: überarbeitet
		Titel: MrFlexySMPs Folded Horn Hybrid **Verstrebung 100 × 555**	Zeichnungsnr.: FLEXY-09
			Rev.: B · Ausgabedatum: 2026-10-16 · Blatt: 9/25

OPTIONAL

Verstrebungen: können z. B. auch aus Metall gefertigt werden.

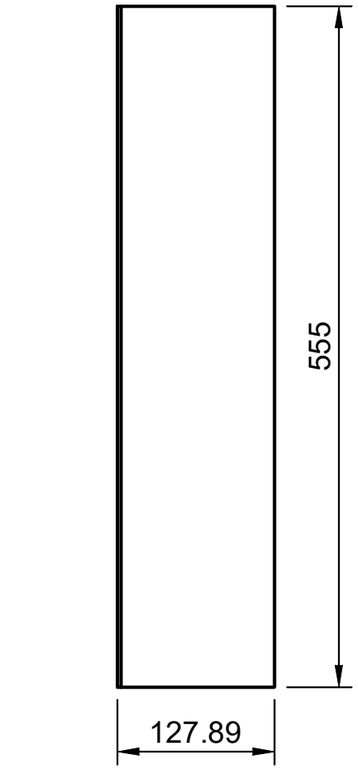


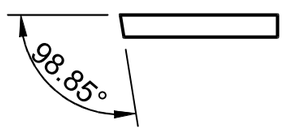


Abteilung: SdWa5 / Technische Referenz: Maßstab 1:5 auf A3		Erstellt von: Oliver Ripper 25.02.2022	Freigegeben von: Stefan Ripper
		Dokumentart: Bauplan	Dokumentstatus: überarbeitet
		Titel: MrFlexySMPs Folded Horn Hybrid **Verstrebung 127,89 × 555**	Zeichnungsnr.: FLEXY-10
			Rev.: B / Ausgabedatum: 2026-10-16 / Blatt: 10/25

OPTIONAL


Verstrebungen: können z. B. auch aus Metall gefertigt werden.

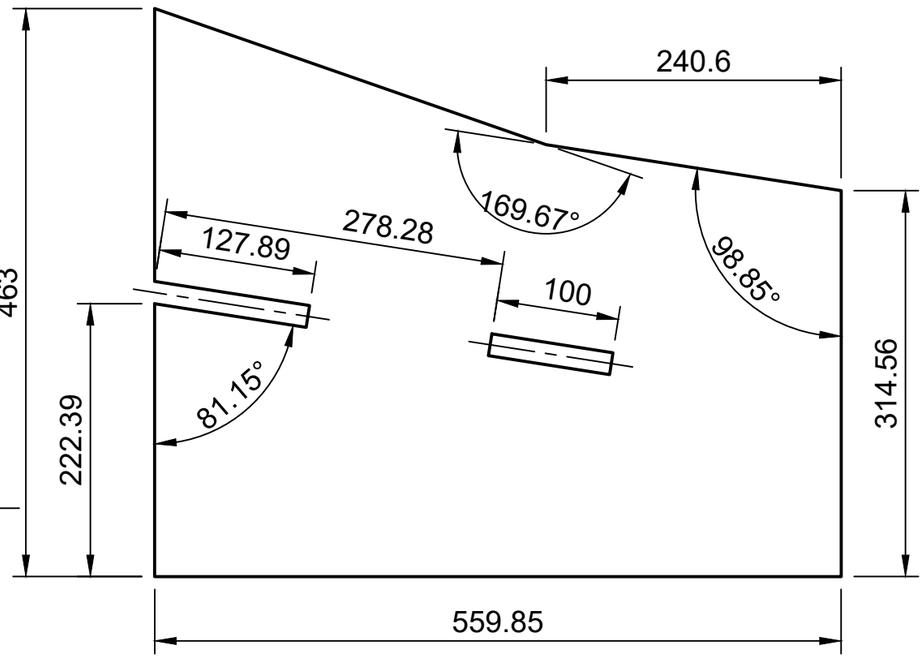




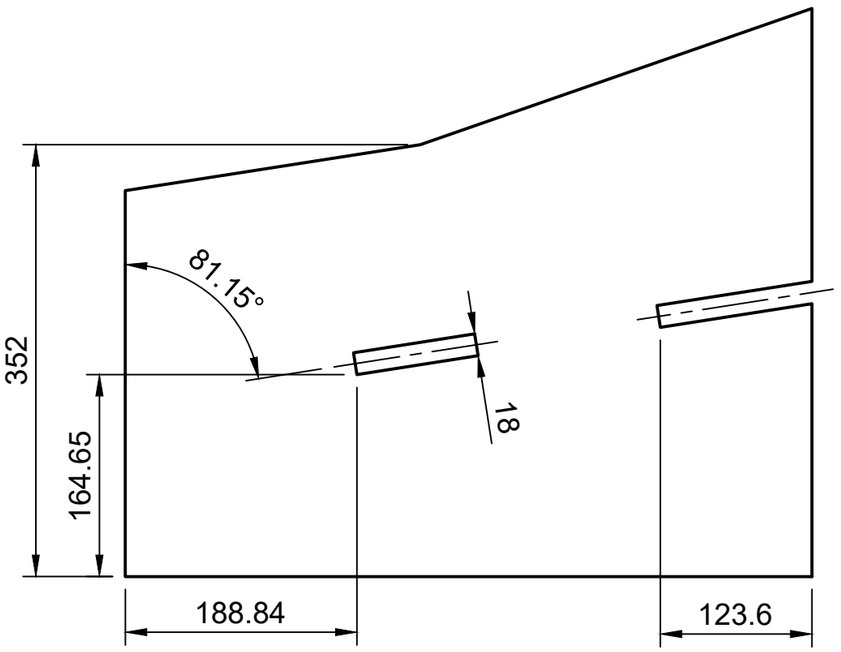



Abteilung	Technische Referenz	Erstellt von	Freigegeben von
SdWa5	Maßstab 1:5 auf A3	Oliver Ripper 25.02.2022	Stefan Ripper
		Dokumentart: Bauplan	Dokumentstatus: überarbeitet
		Titel: MrFlexySMPs Folded Horn Hybrid **Verstrebungsplatte**	Zeichnungsnr.: FLEXY-11
			Rev.: B · Ausgabedatum: 2026-10-16 · Blatt: 11/25

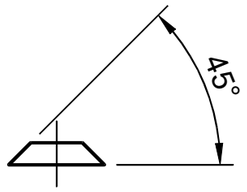

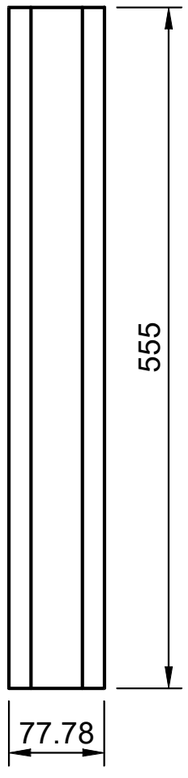

Abteilung: SdWa5	Technische Referenz: Maßstab 1:5 auf A3	Erstellt von: Oliver Ripper 25.02.2022	Freigegeben von: Stefan Ripper
		Dokumentart: Bauplan	Dokumentstatus: überarbeitet
		Titel: MrFlexySMPs Folded Horn Hybrid **Leiste 77,78 × 555**	Zeichnungsnr.: FLEXY-12
			Rev.: B / Ausgabedatum: 2026-10-16 / Blatt: 12/25

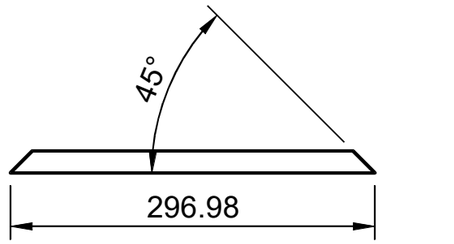


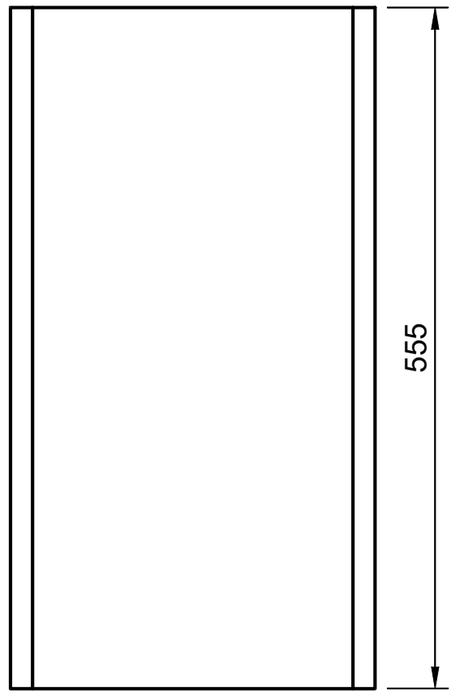

Abteilung	Technische Referenz	Erstellt von	Freigegeben von
SdWa5	Maßstab 1:5 auf A3	Oliver Ripper 25.02.2022	Stefan Ripper
		Dokumentart: Bauplan	Dokumentstatus: überarbeitet
		Titel: MrFlexySMPs Folded Horn Hybrid **Platte 296,98 × 555**	Zeichnungsnr.: FLEXY-13
			Rev.: B · Ausgabedatum: 2026-10-16 · Blatt: 13/25


OPTIONAL

Die Deckel werden aus der oberen Platte (Blatt 6) ausgeschnitten.

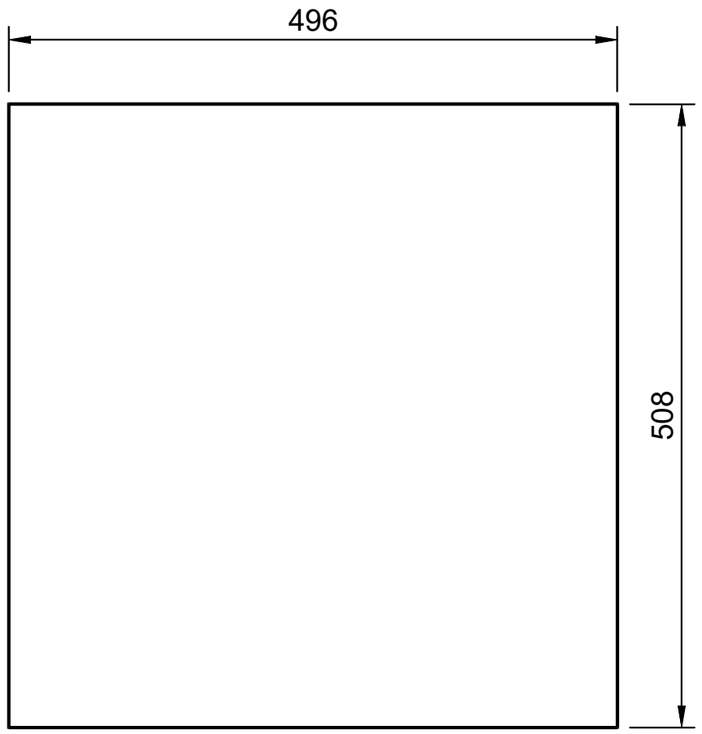


Abteilung: SdWa5	Technische Referenz: Maßstab 1:5 auf A3	Erstellt von: Oliver Ripper 25.02.2022	Freigegeben von: Stefan Ripper
		Dokumentart: Bauplan	Dokumentstatus: überarbeitet
		Titel: MrFlexySMPs Folded Horn Hybrid **Deckel 496 × 508**	Zeichnungsnr.: FLEXY-14
			Rev.: B / Ausgabedatum: 2026-10-16 / Blatt: 14/25


x2

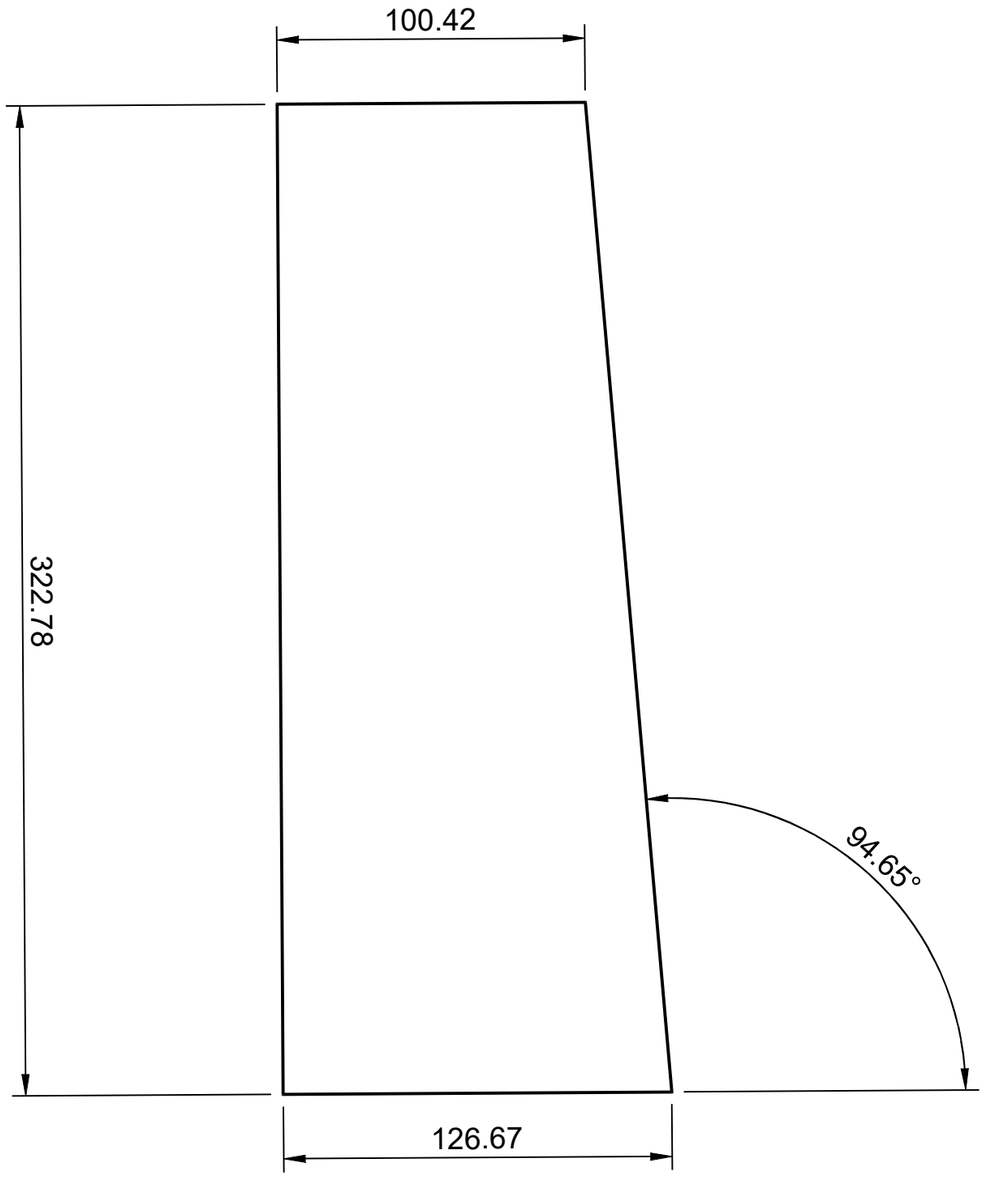

Abteilung	Technische Referenz	Erstellt von	Freigegeben von
SdWa5	Maßstab 1:2 auf A3	Oliver Ripper 25.02.2022	Stefan Ripper
		Dokumentart: Bauplan	Dokumentstatus: überarbeitet
		Titel: MrFlexySMPs Folded Horn Hybrid **Trapez 322,78 (2×)**	Zeichnungsnr.: FLEXY-15
			Rev.: B · Ausgabedatum: 2026-10-16 · Blatt: 15/25

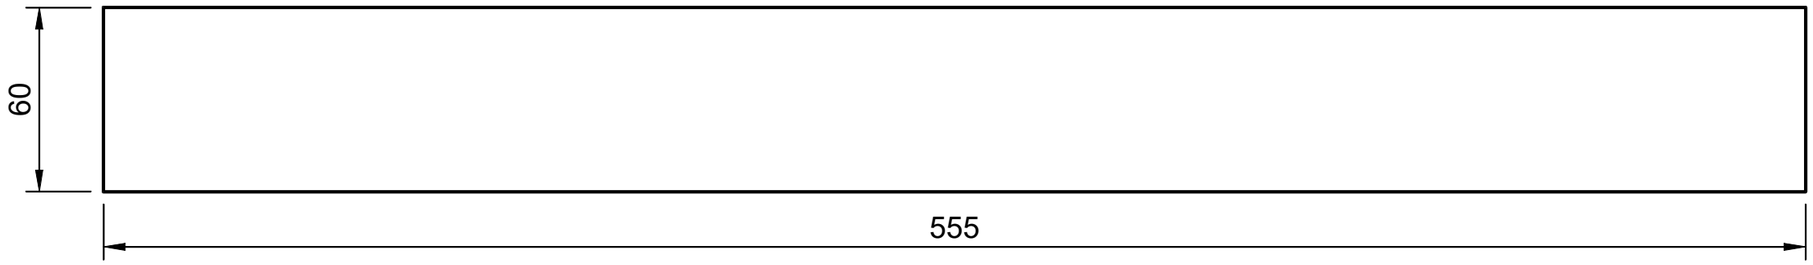



Abteilung: SdWa5	Technische Referenz: Maßstab 1:2 auf A3	Erstellt von: Oliver Ripper 25.02.2022	Freigegeben von: Stefan Ripper
		Dokumentart: Bauplan	Dokumentstatus: überarbeitet
		Titel: MrFlexySMPs Folded Horn Hybrid **Leiste 60 × 555**	Zeichnungsnr.: FLEXY-16
			Rev.: B · Ausgabedatum: 2026-10-16 · Blatt: 16/25

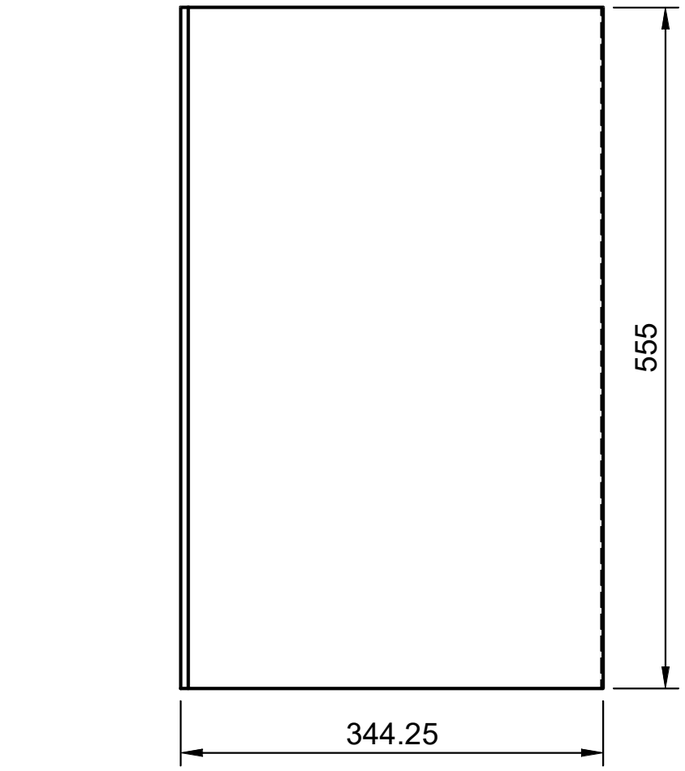




Abteilung	Technische Referenz	Erstellt von	Freigegeben von
SdWa5	Maßstab 1:5 auf A3	Oliver Ripper 25.02.2022	Stefan Ripper
		Dokumentart: Bauplan	Dokumentstatus: überarbeitet
		Titel: MrFlexySMPs Folded Horn Hybrid **Platte 344,25 × 555**	Zeichnungsnr.: FLEXY-17
			Rev.: B · Ausgabedatum: 2026-10-16 · Blatt: 17/25

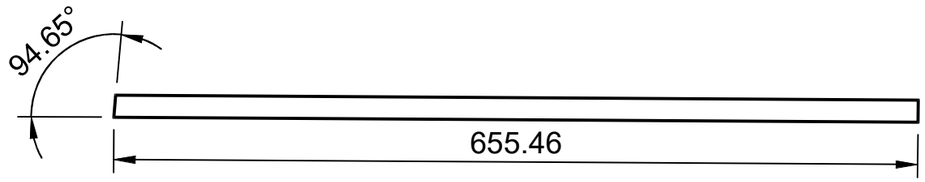


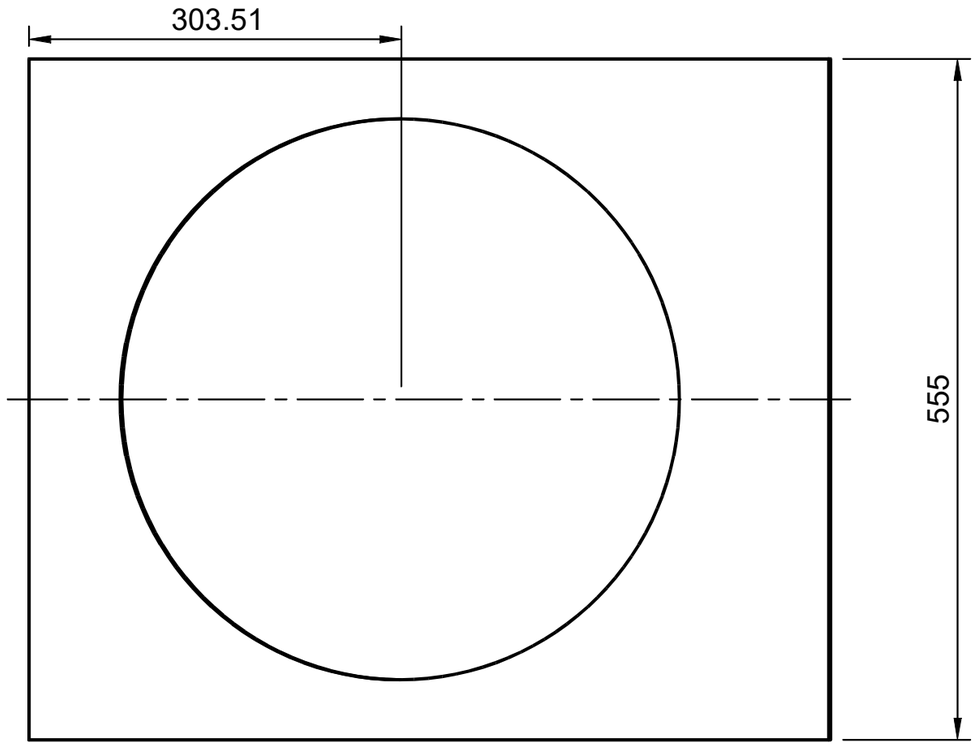

Abteilung	Technische Referenz	Erstellt von	Freigegeben von
SdWa5	Maßstab 1:5 auf A3	Oliver Ripper 25.02.2022	Stefan Ripper
		Dokumentart: Bauplan	Dokumentstatus: überarbeitet
		Titel: MrFlexySMPs Folded Horn Hybrid	Zeichnungsnr.: FLEXY-18
		Schallwand mit Treiberausschnitt	Rev.: B · Ausgabedatum: 2026-10-16 · Blatt: 18/25

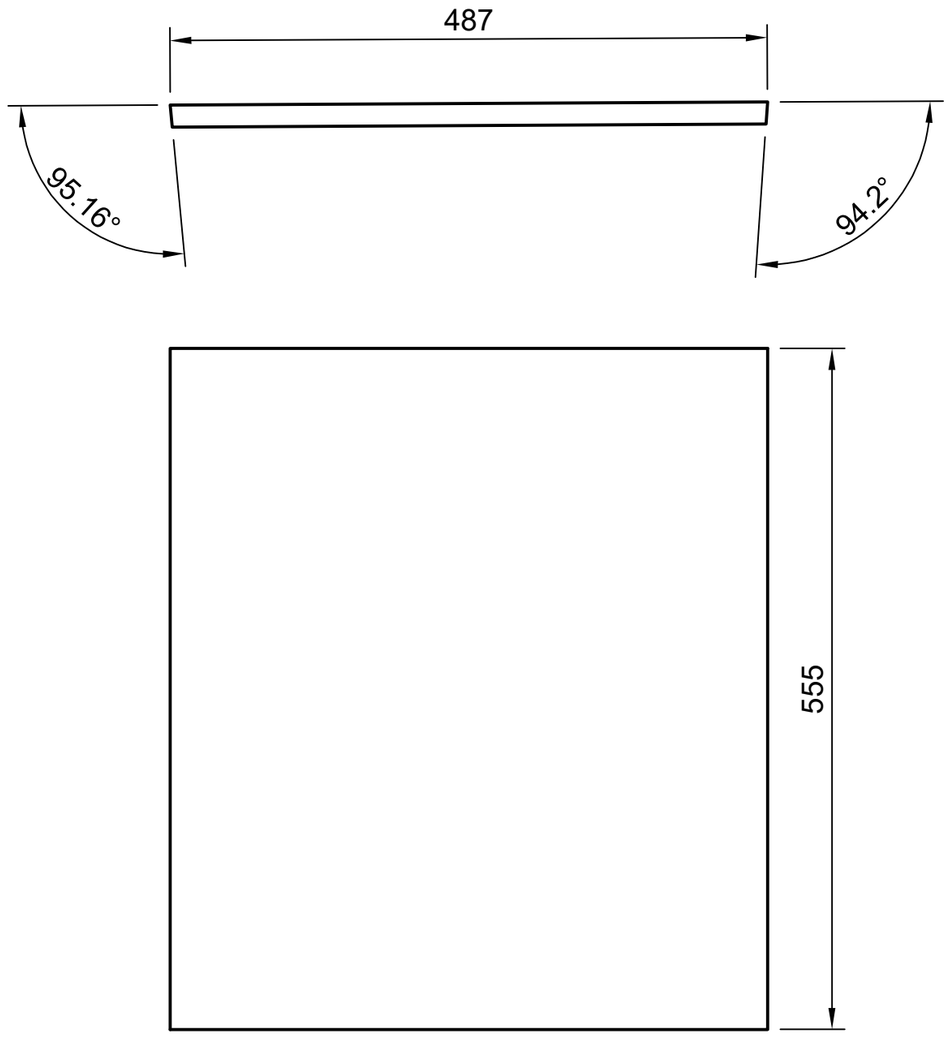


Abteilung: SdWa5	Technische Referenz: Maßstab 1:5 auf A3	Erstellt von: Oliver Ripper 25.02.2022	Freigegeben von: Stefan Ripper
		Dokumentart: Bauplan	Dokumentstatus: überarbeitet
		Titel: MrFlexySMPs Folded Horn Hybrid **Platte 487 × 555**	Zeichnungsnr.: FLEXY-19
			Rev.: B / Ausgabedatum: 2026-10-16 / Blatt: 19/25

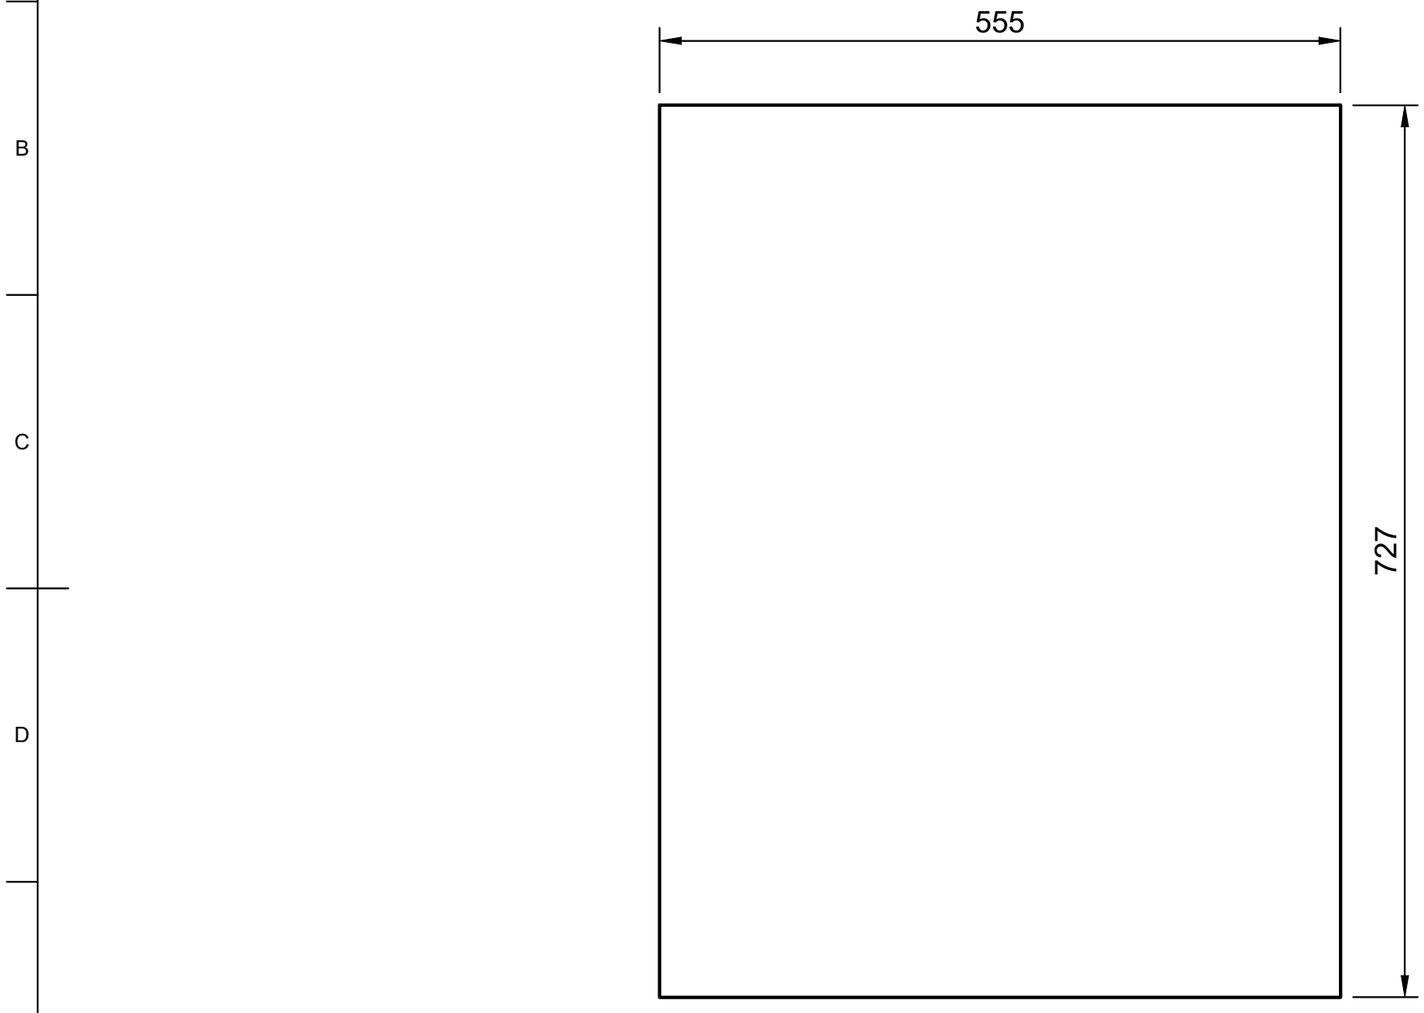


Abteilung	Technische Referenz	Erstellt von	Freigegeben von
SdWa5	Maßstab 1:5 auf A3	Oliver Ripper 25.02.2022	Stefan Ripper
		Dokumentart: Bauplan	Dokumentstatus: überarbeitet
		Titel: MrFlexySMPs Folded Horn Hybrid **Platte 555 × 727**	Zeichnungsnr.: FLEXY-20
			Rev.: B · Ausgabedatum: 2026-10-16 · Blatt: 20/25


x2

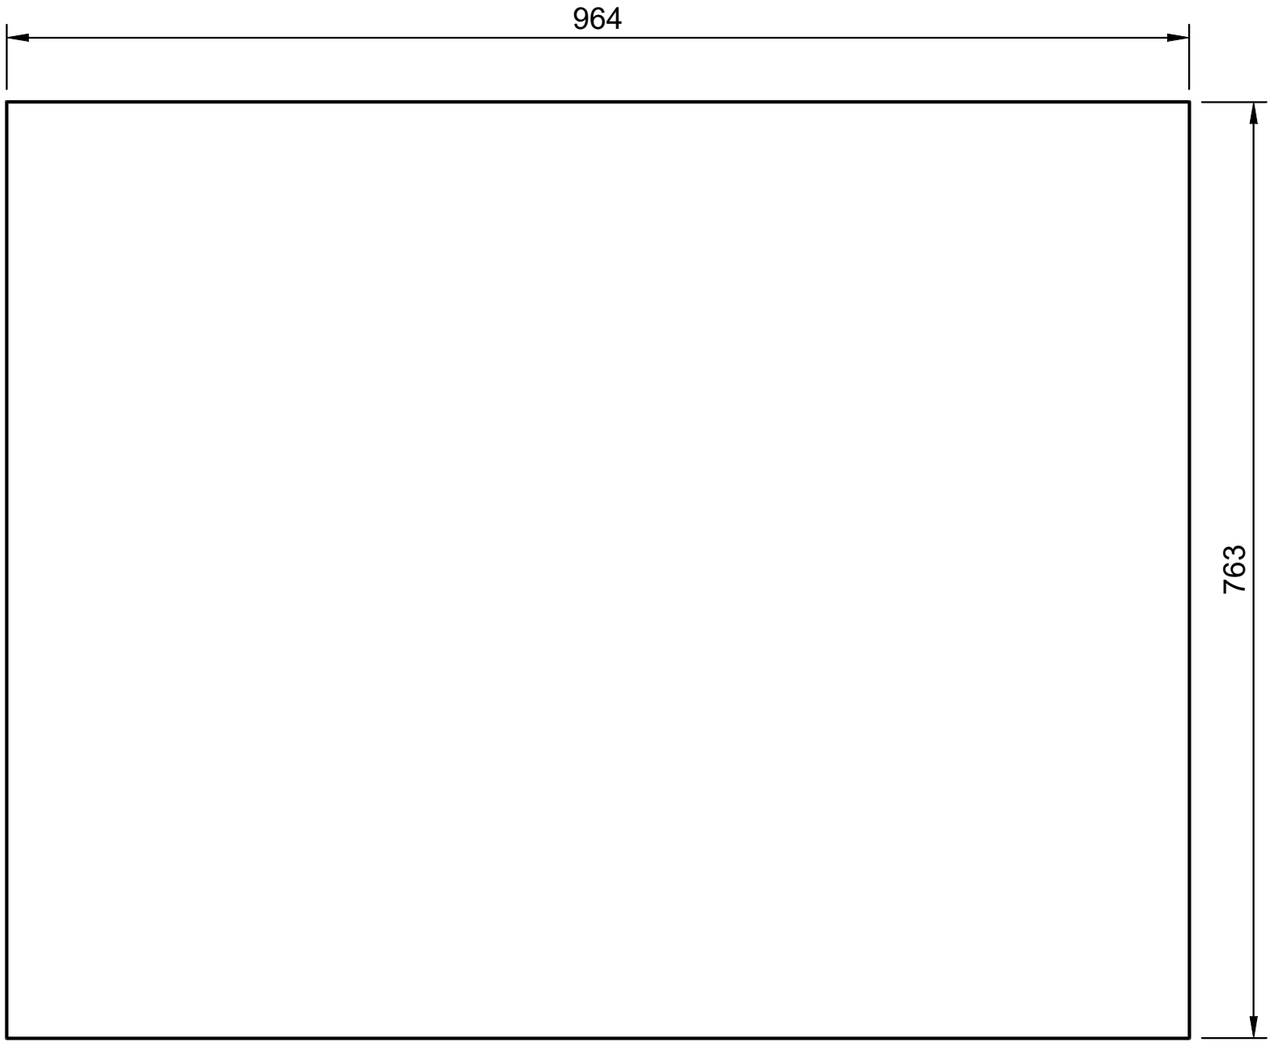


Abteilung	Technische Referenz	Erstellt von	Freigegeben von
SdWa5	Maßstab 1:5 auf A3	Oliver Ripper 25.02.2022	Stefan Ripper
		Dokumentart: Bauplan	Dokumentstatus: überarbeitet
		Titel: MrFlexySMPs Folded Horn Hybrid **Seitenwand (2×)**	Zeichnungsnr.: FLEXY-21
			Rev.: B · Ausgabedatum: 2026-10-16 · Blatt: 21/25

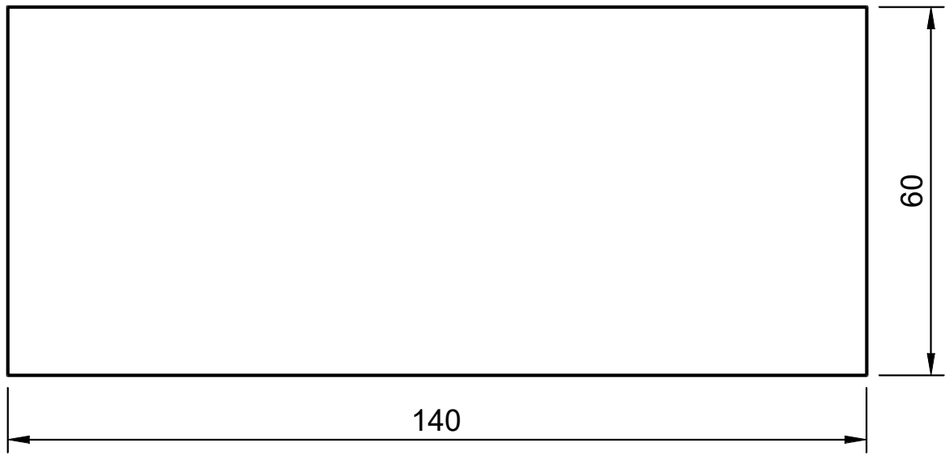



Abteilung	Technische Referenz	Erstellt von	Freigegeben von
SdWa5	Maßstab 1:1 auf A3	Oliver Ripper 25.02.2022	Stefan Ripper
		Dokumentart: Bauplan	Dokumentstatus: überarbeitet
		Titel: MrFlexySMPs Folded Horn Hybrid **Klotz 140 × 60**	Zeichnungsnr.: FLEXY-22
			Rev.: B · Ausgabedatum: 2026-10-16 · Blatt: 22/25

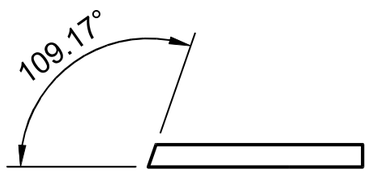

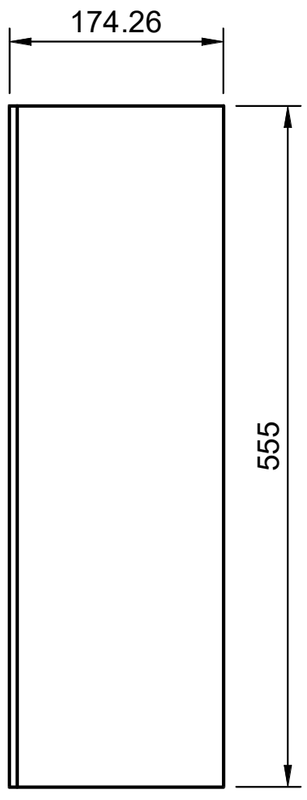


Abteilung	Technische Referenz	Erstellt von	Freigegeben von
SdWa5	Maßstab 1:5 auf A3	Oliver Ripper 25.02.2022	Stefan Ripper
		Dokumentart: Bauplan	Dokumentstatus: überarbeitet
		Titel: MrFlexySMPs Folded Horn Hybrid **Platte 174,26 × 555**	Zeichnungsnr.: FLEXY-23
			Rev.: B · Ausgabedatum: 2026-10-16 · Blatt: 23/25

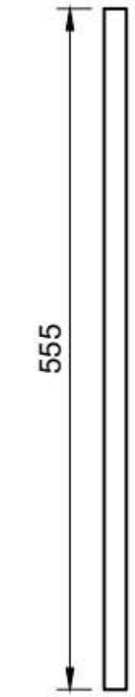

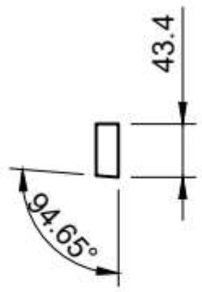

Abteilung: SdWa5	Technische Referenz: Maßstab 1:5 auf A3	Erstellt von: Oliver Ripper 25.02.2022	Freigegeben von: Stefan Ripper
		Dokumentart: Bauplan	Dokumentstatus: überarbeitet
		Titel: MrFlexySMPs Folded Horn Hybrid **Leiste 555**	Zeichnungsnr.: FLEXY-24
			Rev.: B / Ausgabedatum: 2026-10-16 / Blatt: 24/25

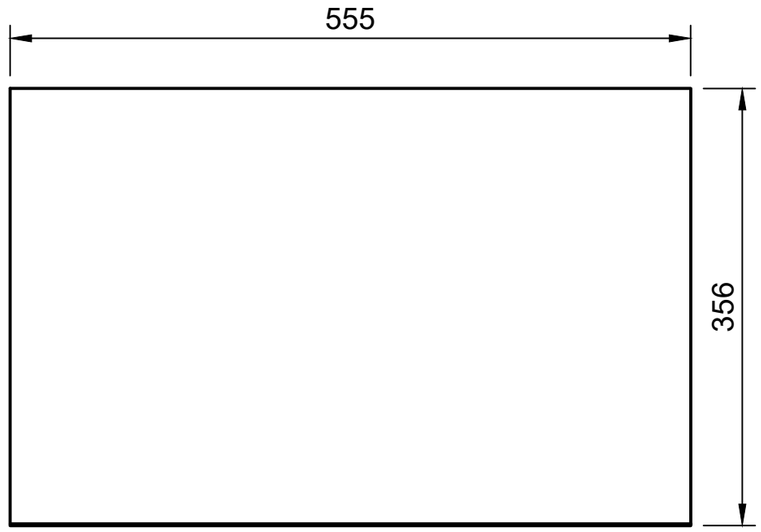

Abteilung	Technische Referenz	Erstellt von	Freigegeben von
SdWa5	Maßstab 1:5 auf A3	Oliver Ripper 25.02.2022	Stefan Ripper
		Dokumentart: Bauplan	Dokumentstatus: überarbeitet
		Titel: MrFlexySMPs Folded Horn Hybrid **Platte 555 × 356**	Zeichnungsnr.: FLEXY-25
			Rev.: B · Ausgabedatum: 2026-10-16 · Blatt: 25/25